A区首层平面图 1:200

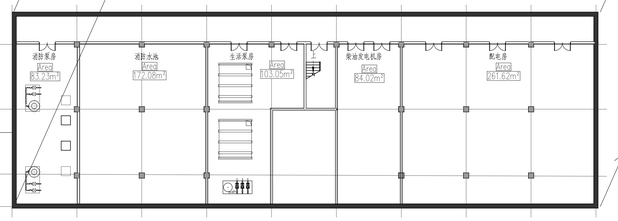

A区负一层平面图 1:200

中国建筑西南设计研究院有限公司
CHINA SOUTHWEST ARCHITECTURAL DESIGN AND RESEARCH INSTITUTE CORP.LTD

注册执业章
REGISTERED PRACTICE SIGNET

姓名 NAME
注册印章号 REGISTERED SIGNET NO.
注册证书号 REGISTERED CERTIFICATE NO.

建设单位:（CLIENT:）

设计项目名 PROJECT NAME

子项名称 SUB PROJECT

图名:（DWG. NAME:）

单位 unit: 比例 scale:

设计总负责人 PROJECT LEADER
专业负责人 DIVISION CHIEF
设 计 DESIGNED BY
校 对 PROCEEDED BY
审 核 CHECKED BY
审 定 APPROVED BY
设计项目号 PROJECT NO.
图别 DWG TYPE
图号 DWG. NO.
版本号 VER.
日期 DATE 年 月